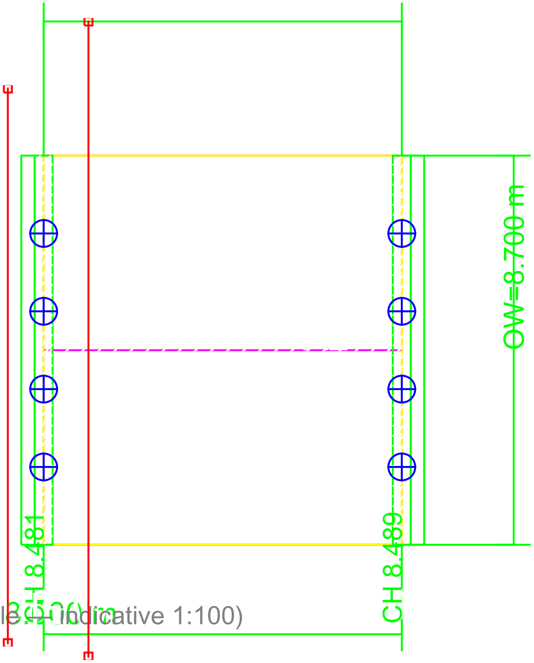

A-A

B-B

(Not to Scale — indicative 1:100)

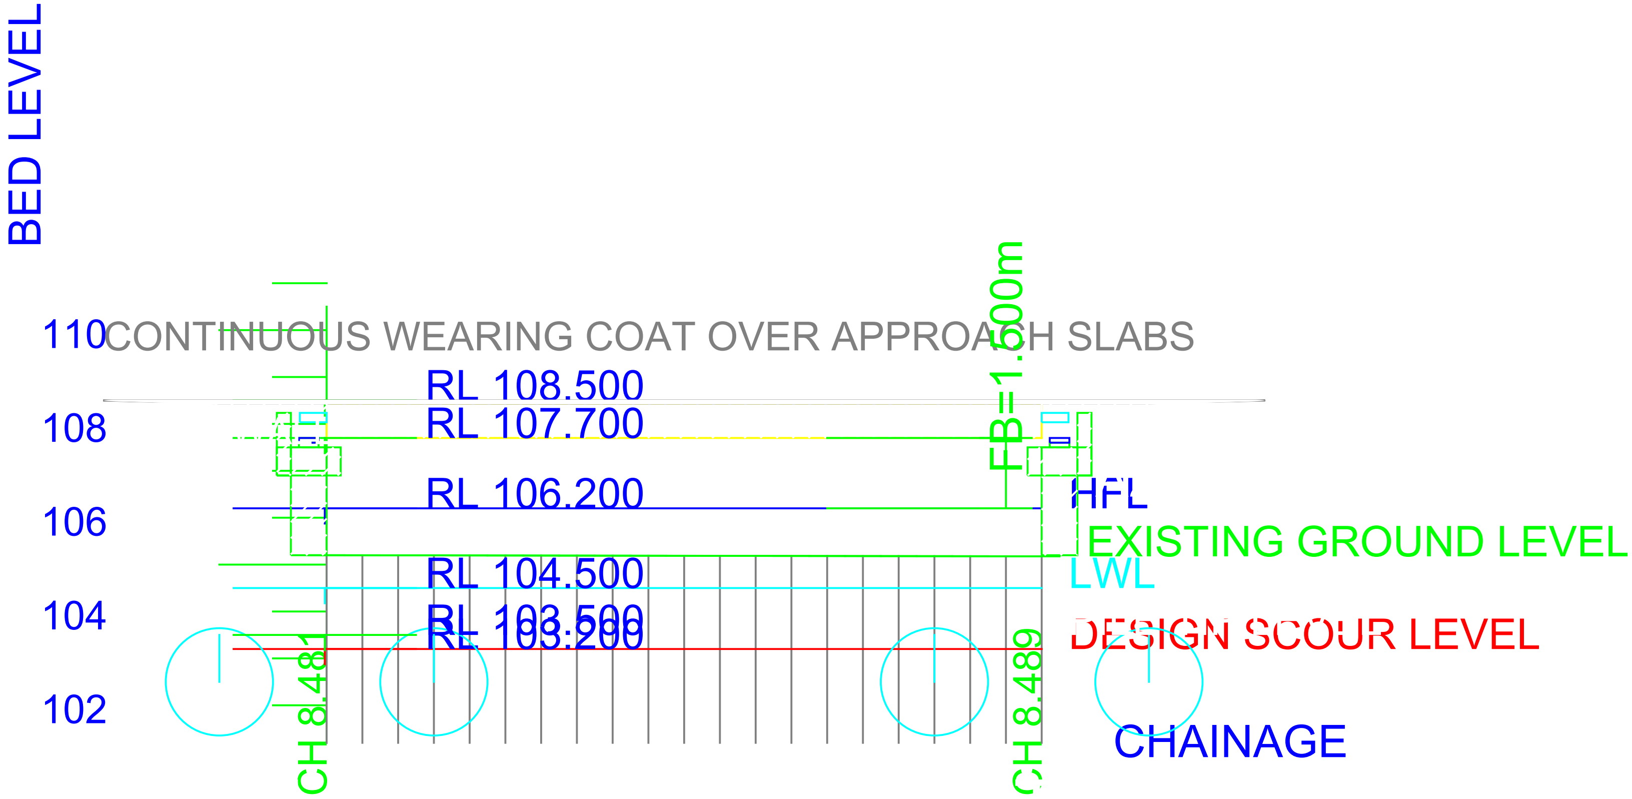

(Not to Scale — indicative)

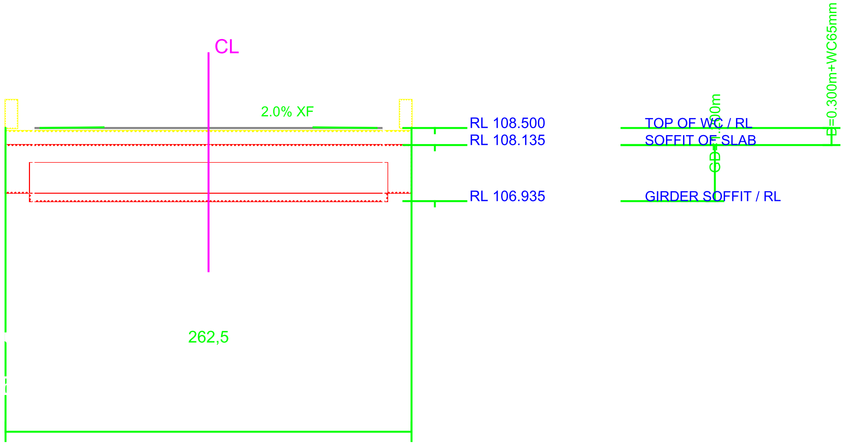
CL
2.0% XF
RL 108.500
RL 108.135
RL 106.935
TOP OF WC / RL
SOFFIT OF SLAB
GIRDER SOFFIT / RL
GD=[illegible]00m
D=0.300m+WC65mm
262,5

DESIGN SCOUR RL 103.200

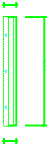

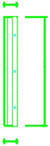

[illegible]

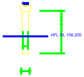

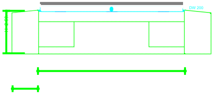

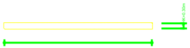

QA-ABT-CAP-DEF	Abutment cap depth	0 mm	>= 450 mm	OK
QA-ABT-CAP-PR	Cap projection front/rear	0/0 mm	100-250 / 250-600 mm	OK
QA-DW-THK	Dirt wall thickness	0 mm	>= 250 mm	OK
QA-DW-TOP	Dirt wall to slab soffit	0.73 m	>= 0.30 m	OK
QA-DW-WEEP	Weep holes provided	3	1 per 3 m	OK
QA-ABT-OT	Overturning FOS	0.30	>= 1.40	FAIL
QA-ABT-SL	Sliding FOS	0.68	>= 1.40	FAIL
QA-ABT-BRG	Base pressure	720.94 kPa	<= 250.00 kPa	FAIL

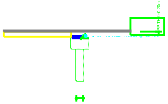

[illegible]

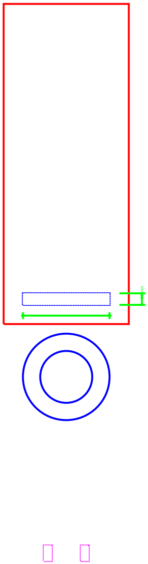
mm
GAP

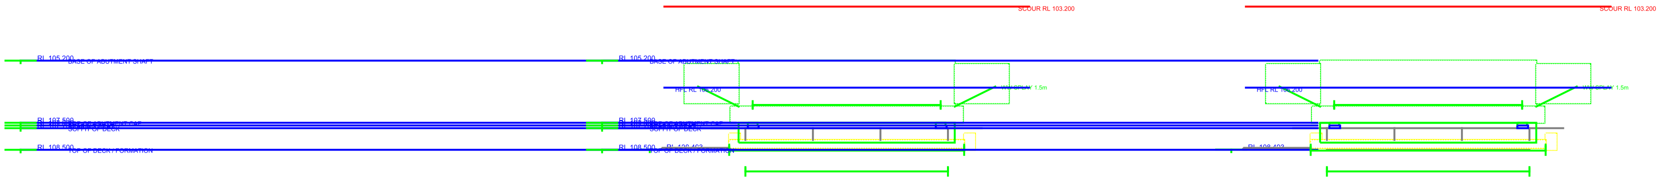
SCOUR RL 103.200
SCOUR RL 103.200
RL 105.200 BASE OF ABUTMENT SHAFT
RL 105.200 BASE OF ABUTMENT SHAFT
HFL RL 106.200
WW SPLAY 1.5m
HFL RL 106.200
WW SPLAY 1.5m
RL 107.500 TOP OF ABUTMENT CAP
SOFFIT OF DECK
RL 107.500 TOP OF ABUTMENT CAP
SOFFIT OF DECK
RL 108.500 TOP OF DECK / FORMATION
RL 108.500 TOP OF DECK / FORMATION
RL 108.403
RL 108.403

QA-ABT-C	Abutment cap depth	0 mm	>= 450 mm	OK
QA-ABT-C	Cap projection front/rear	0/0 mm	100-250 / 250-600 mm	OK
QA-DW-TI	Dirt wall thickness	0 mm	>= 250 mm	OK
QA-DW-T	Dirt wall to slab soffit	0.73 m	>= 0.30 m	OK
QA-DW-W	Weep holes provided	3	1 per 3 m	OK
QA-ABT-C	Overturning FOS	0.30	>= 1.40	FAIL
QA-ABT-S	Sliding FOS	0.68	>= 1.40	FAIL
QA-ABT-E	Base pressure	720.94 kPa	<= 250.00 kPa	FAIL

(Not to Scale – indicative) TER (BEYOND)