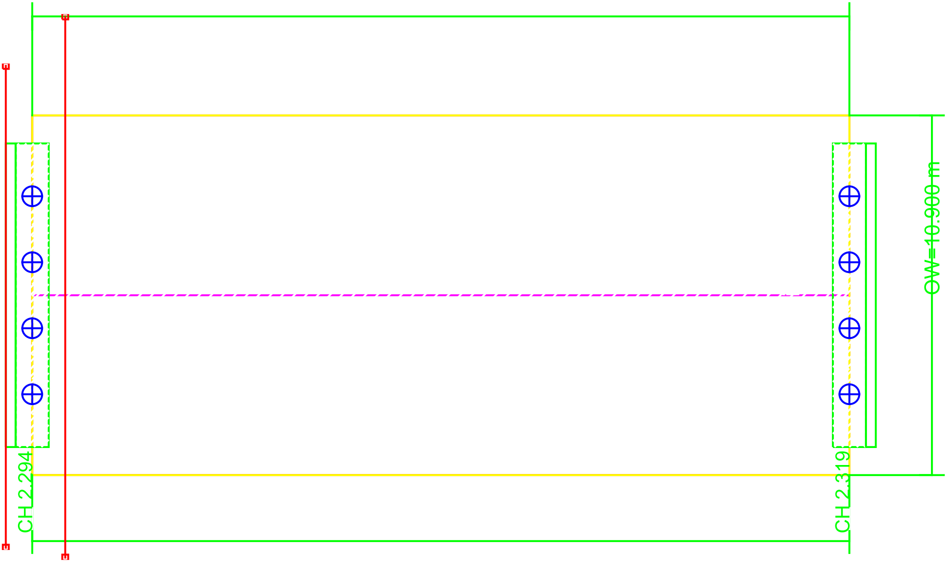

A-A

B-B

[illegible] = 24.750 m

(Not to Scale — indicative 1:100)

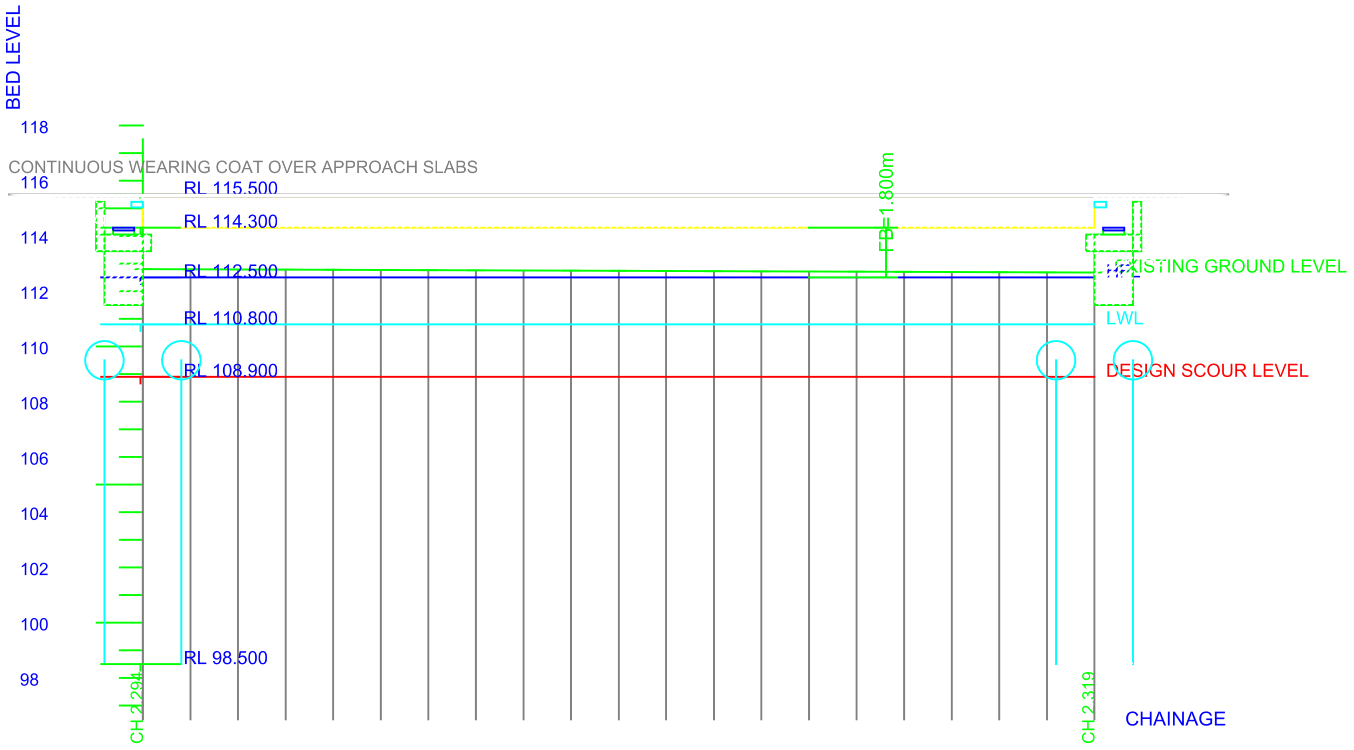

(Not to Scale — indicative)

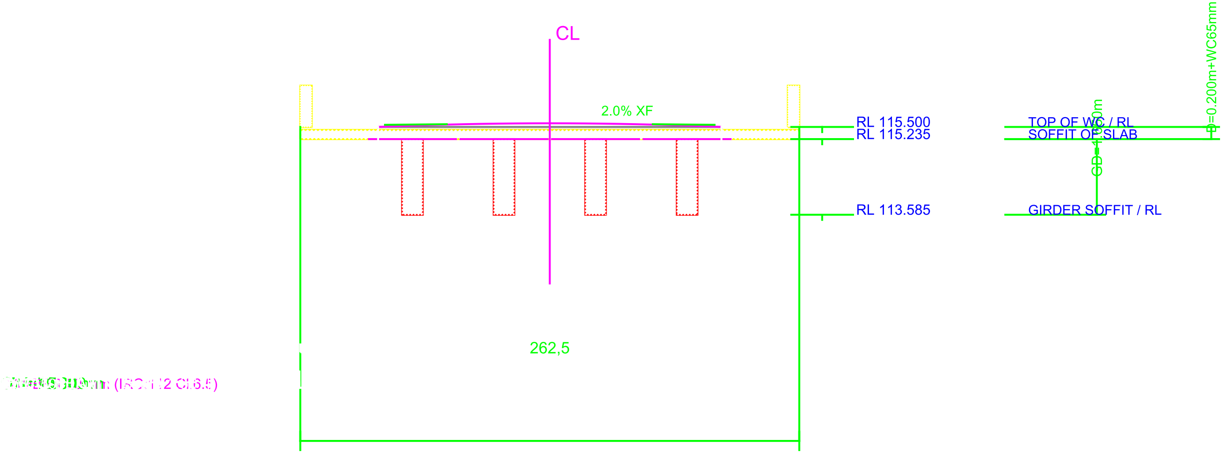
CL
2.0% XF
RL 115.500
RL 115.235
RL 113.585
TOP OF WC / RL
SOFFIT OF SLAB
GIRDER SOFFIT / RL
GD=1.650m
D=0.200m+WC65mm
262,5

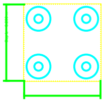

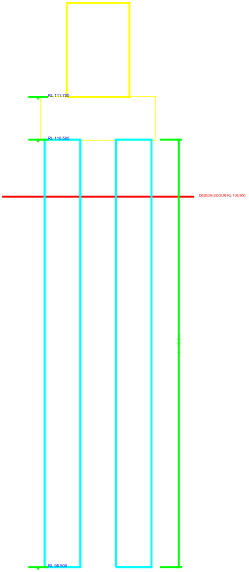
RL 111.700
RL 110.500
DESIGN SCOUR RL 108.900
RL 98.500

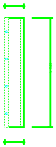

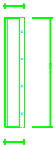

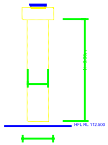

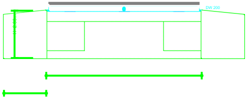

QA-ABT-CAP-DEP	Abutment cap depth	0 mm	>= 450 mm	OK
QA-ABT-CAP-PRO	Cap projection front/rear	0/0 mm	100-250 / 250-600 mm	OK
QA-DW-THK	Dirt wall thickness	0 mm	>= 250 mm	OK
QA-DW-TOP	Dirt wall to slab soffit	1.19 m	>= 0.30 m	OK
QA-DW-WEEP	Weep holes provided	4	1 per 3 m	OK
QA-ABT-OT	Overturning FOS	1.36	>= 1.40	FAIL
QA-ABT-SL	Sliding FOS	1.39	>= 1.40	FAIL
QA-ABT-BRG	Base pressure	159.91 kPa	<= 350.00 kPa	OK

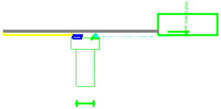

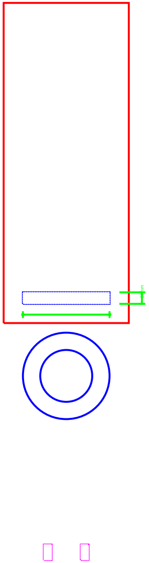

GAP

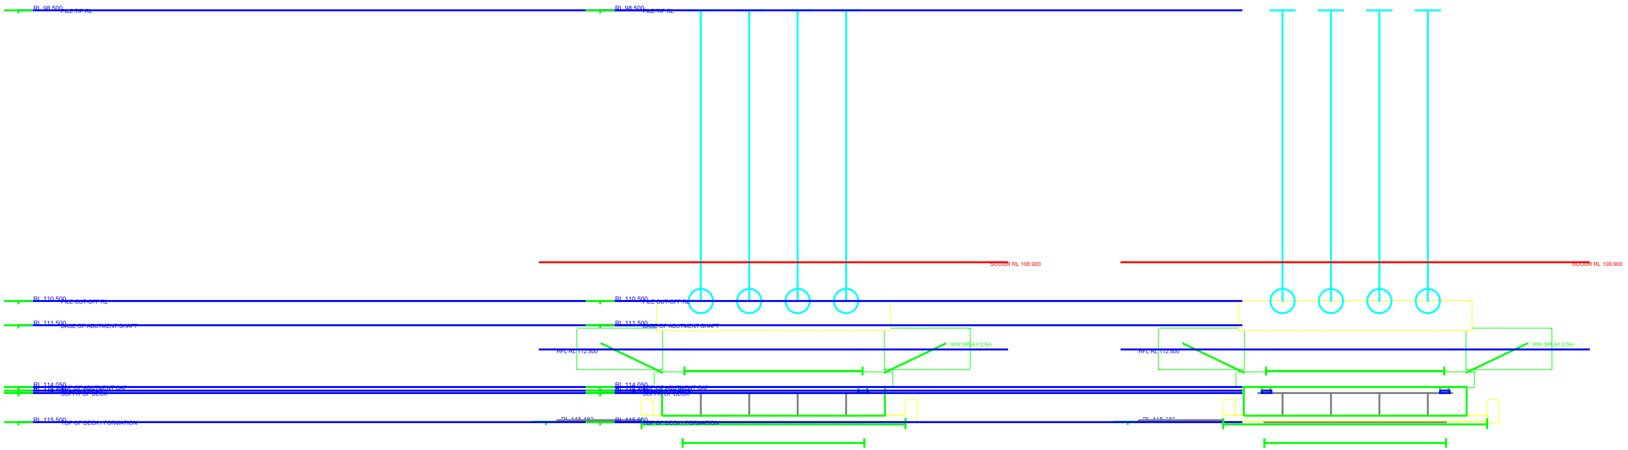

QA-ABT-C/	Abutment cap depth	0 mm	>= 450 mm	OK
QA-ABT-C/	Cap projection front/rear	0/0 mm	100-250 / 250-600 m	OK
QA-DW-TH	Dirt wall thickness	0 mm	>= 250 mm	OK
QA-DW-TO	Dirt wall to slab soffit	1.19 m	>= 0.30 m	OK
QA-DW-WE	Weep holes provided	4	1 per 3 m	OK
QA-ABT-OT	Overturning FOS	1.36	>= 1.40	FAIL
QA-ABT-SL	Sliding FOS	1.39	>= 1.40	FAIL
QA-ABT-BF	Base pressure	159.91 kPa	<= 350.00 kPa	OK

(Not to Scale – indicative) TER (BEYOND)