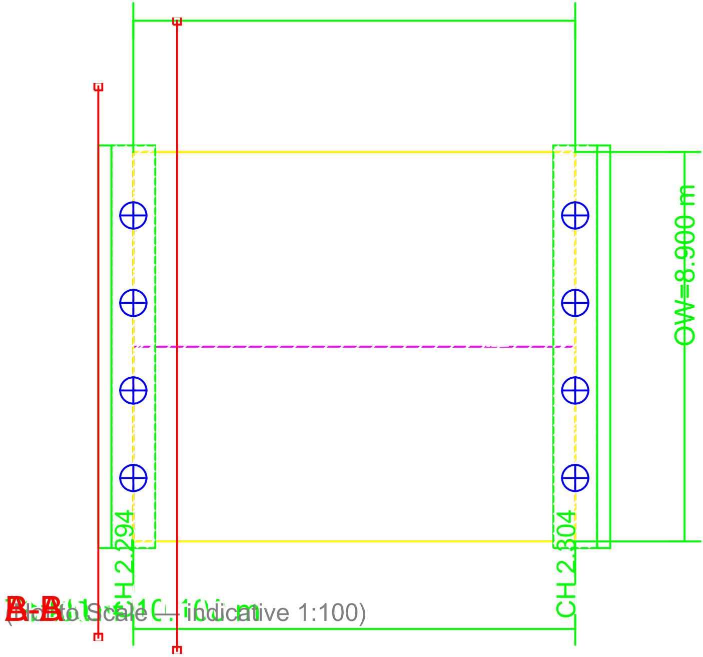

(Not to Scale — indicative 1:100)

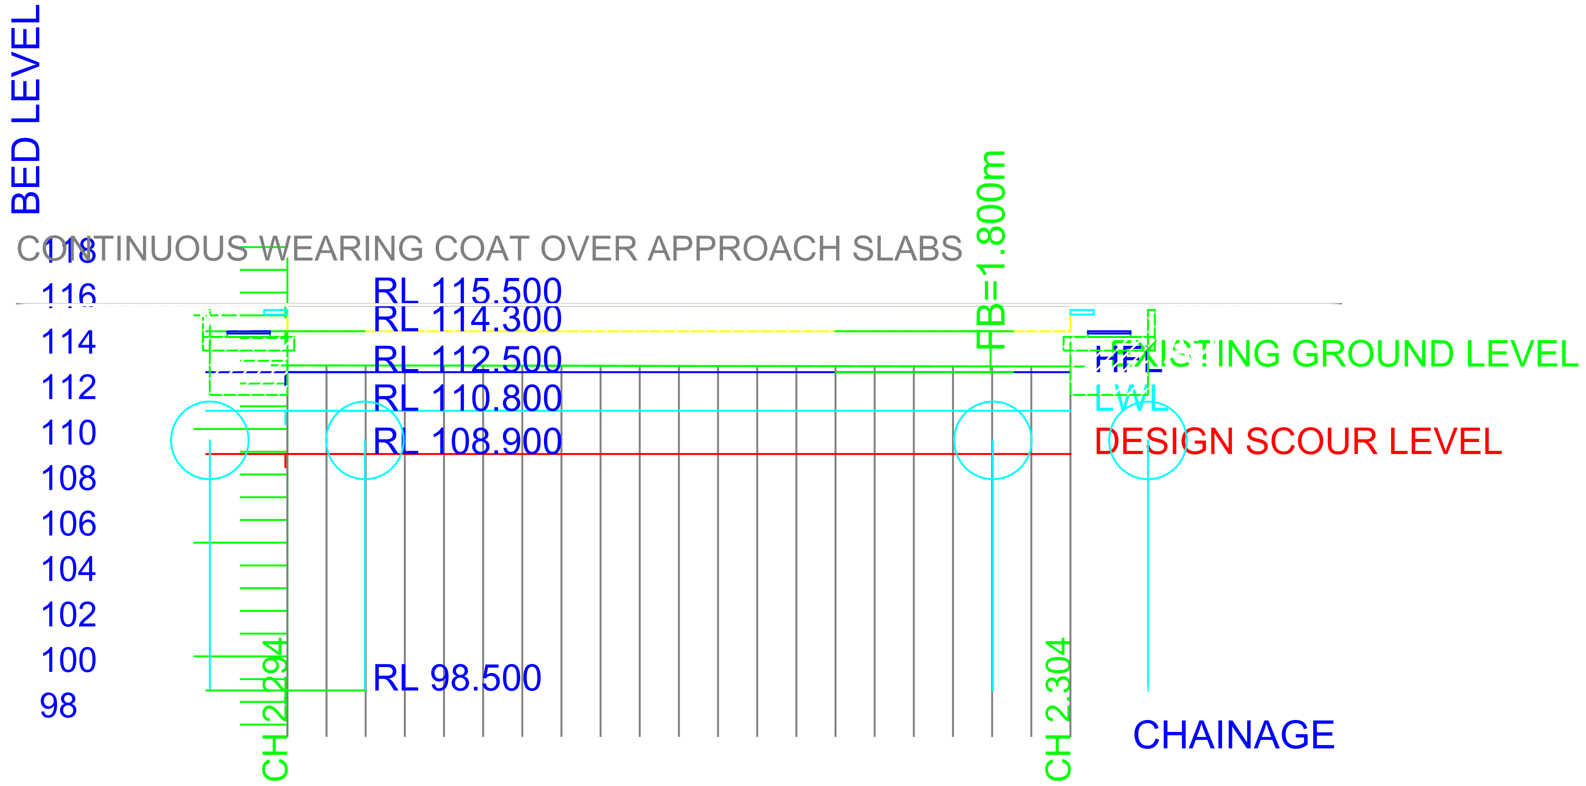

(Not to Scale — indicative)

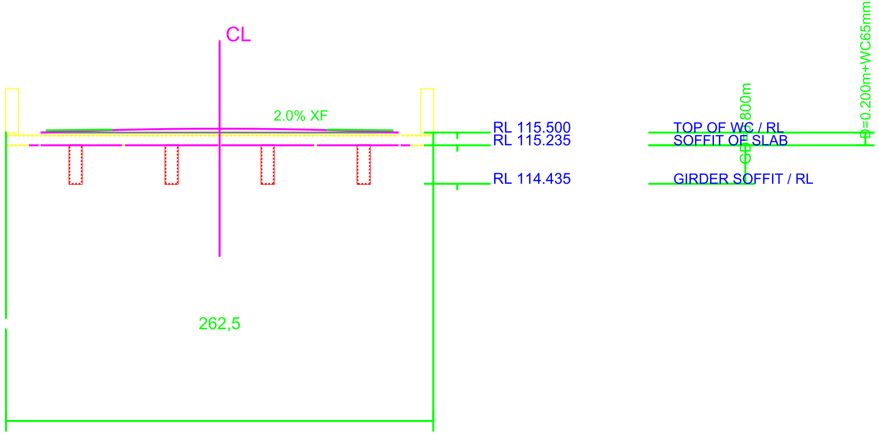

mm (IRC:112 Cl.6.5)

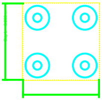

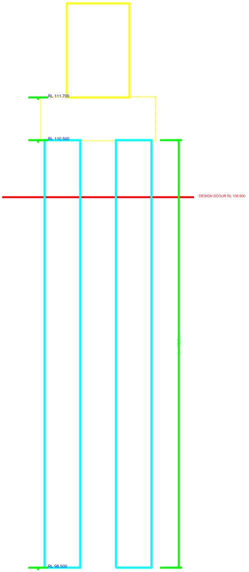
RL 111.700
RL 110.500
DESIGN SCOUR RL 108.900
RL 98.500

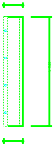

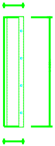

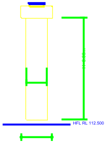

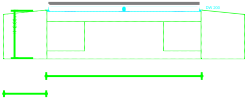

QA-ABT-CAP-DEF	Abutment cap depth	0 mm	>= 450 mm	OK
QA-ABT-CAP-PRC	Cap projection front/rear	0/0 mm	100-250 / 250-600 mm	OK
QA-DW-THK	Dirt wall thickness	0 mm	>= 250 mm	OK
QA-DW-TOP	Dirt wall to slab soffit	1.19 m	>= 0.30 m	OK
QA-DW-WEEP	Weep holes provided	4	1 per 3 m	OK
QA-ABT-OT	Overturning FOS	1.36	>= 1.40	FAIL
QA-ABT-SL	Sliding FOS	1.39	>= 1.40	FAIL
QA-ABT-BRG	Base pressure	159.91 kPa	<= 350.00 kPa	OK

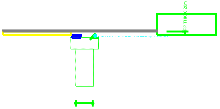

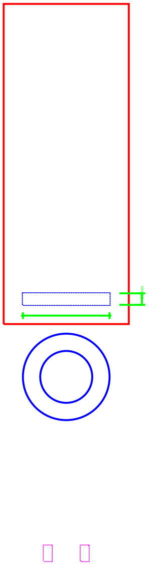

GAP

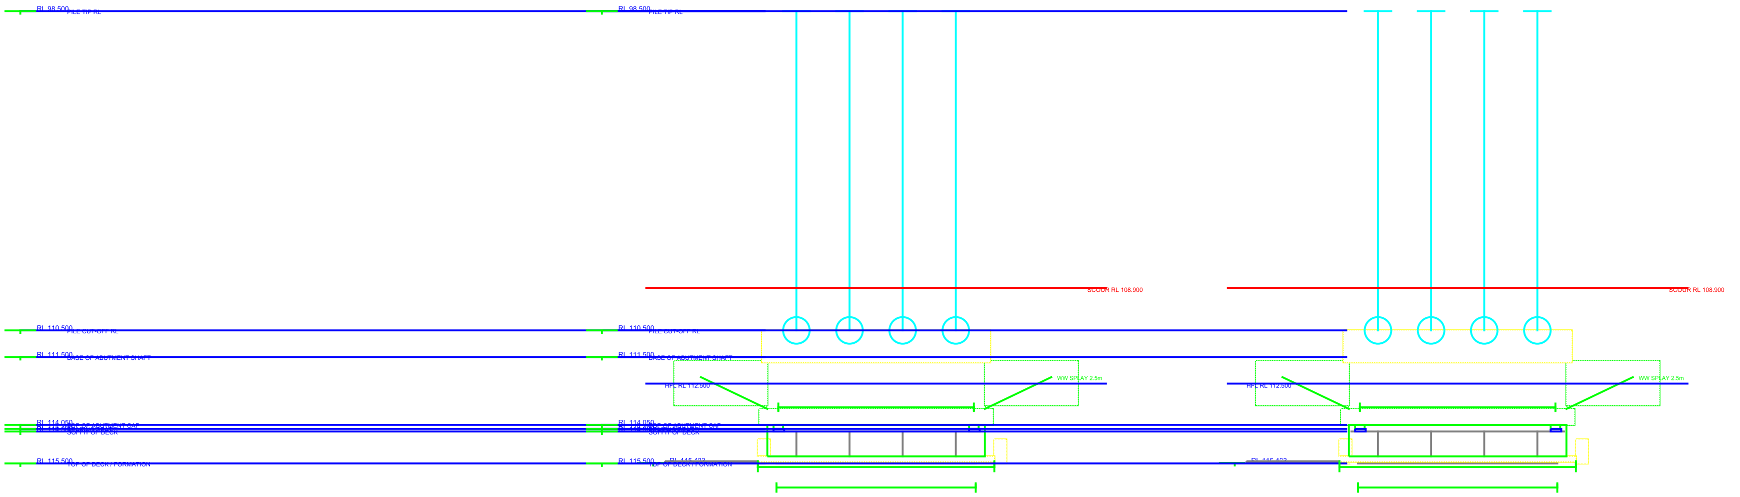
RL 98.500 PILE TIP RL
RL 98.500 PILE TIP RL
SCOUR RL 108.900
SCOUR RL 108.900
RL 110.500 PILE CUT-OFF RL
RL 110.500 PILE CUT-OFF RL
RL 111.500 BASE OF ABUTMENT SHAFT
RL 111.500 BASE OF ABUTMENT SHAFT
HFL RL 112.500
WW SPLAY 2.5m
HFL RL 112.500
WW SPLAY 2.5m
RL 114.050 BASE OF ABUTMENT CAP
SOFFIT OF DECK
RL 114.050 BASE OF ABUTMENT CAP
SOFFIT OF DECK
RL 115.500 TOP OF DECK / FORMATION
RL 115.500 TOP OF DECK / FORMATION
RL 115.423
RL 115.423

QA-ABT-C	Abutment cap depth	0 mm	>= 450 mm	OK
QA-ABT-C	Cap projection front/rear	0/0 mm	100-250 / 250-600 mm	OK
QA-DW-TI	Dirt wall thickness	0 mm	>= 250 mm	OK
QA-DW-T(	Dirt wall to slab soffit	1.19 m	>= 0.30 m	OK
QA-DW-W	Weep holes provided	4	1 per 3 m	OK
QA-ABT-C	Overturning FOS	1.36	>= 1.40	FAIL
QA-ABT-S	Sliding FOS	1.39	>= 1.40	FAIL
QA-ABT-B	Base pressure	159.91 kPa	<= 350.00 kPa	OK

(Not to Scale — indicative) TER (BEYOND)