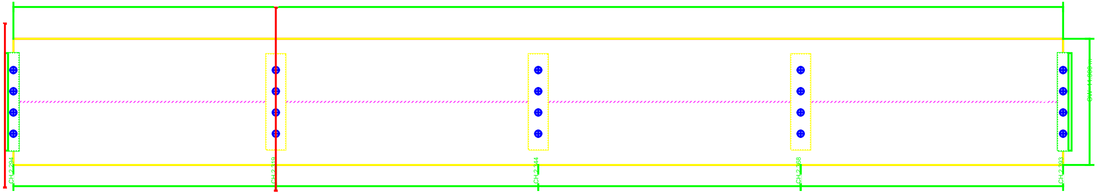
CH 2.294
CH 2.319
CH 2.344
CH 2.368
CH 2.393
OW 11.900 m

B-B [illegible] (Not to Scale — Indicative 1:100)

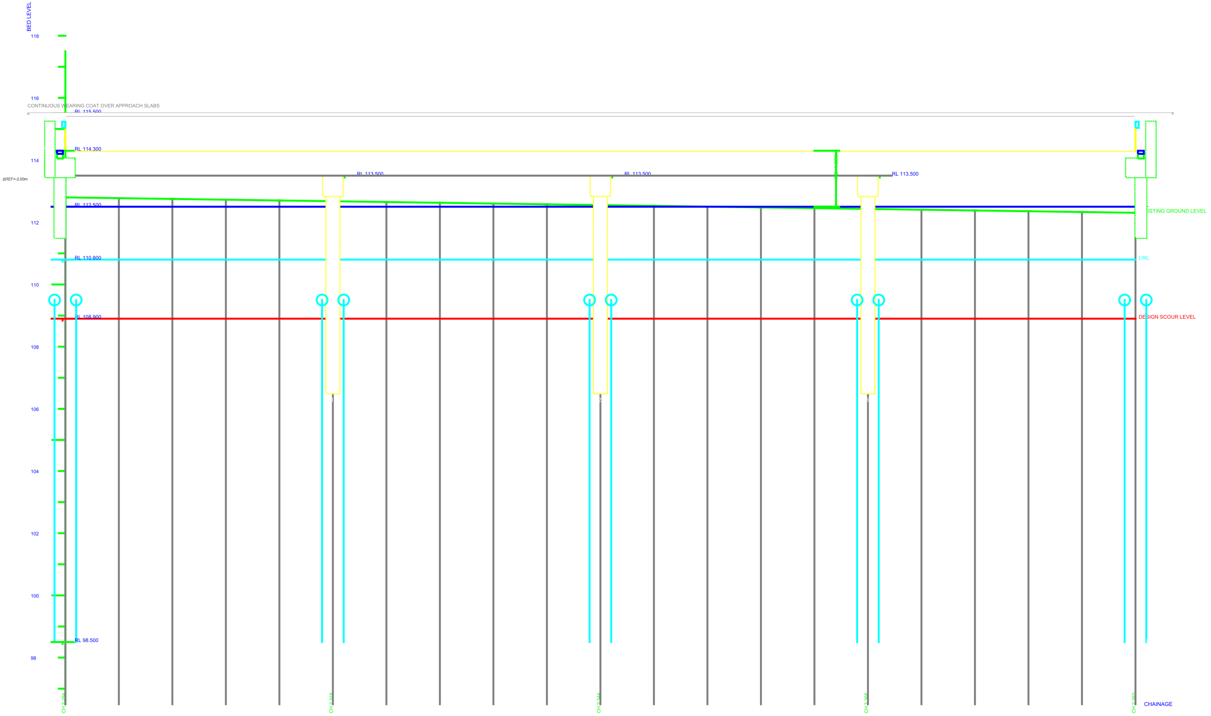
BED LEVEL
118
116
CONTINUOUS WEARING COAT OVER APPROACH SLABS
RL 115.500
RL 114.300
114
ΔREF=-2.00m
RL 113.500
RL 113.500
RL 113.500
RL 112.500
112
EXISTING GROUND LEVEL
RL 110.800
LWL
110
RL 108.900
DESIGN SCOUR LEVEL
108
106
1
2
3
104
102
100
RL 98.500
98
CH 2.294
CH 2.319
CH 2.344
CH 2.368
CH 2.393
CHAINAGE

(Not to Scale — indicative)

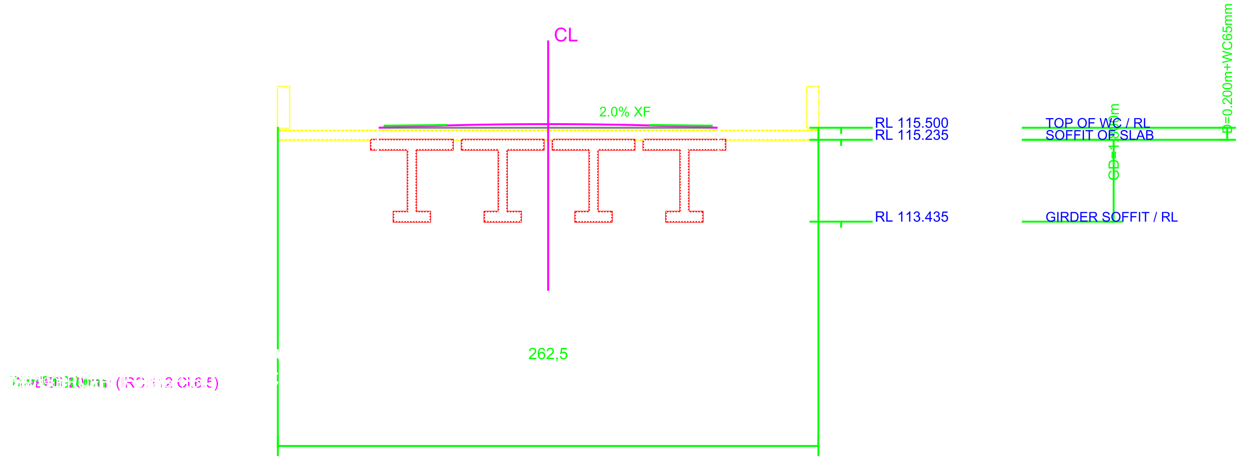
CL
2.0% XF
RL 115.500
RL 115.235
RL 113.435
TOP OF WC / RL
SOFFIT OF SLAB
GIRDER SOFFIT / RL
GD=1.800m
D=0.200m+WC65mm
262,5
(IRC:112 Cl.6.5)

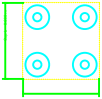

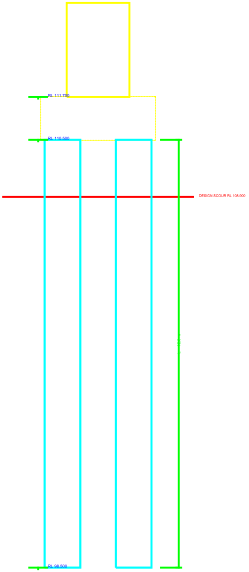
RL 111.700
RL 110.500
DESIGN SCOUR RL 108.900
RL 98.500

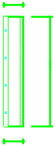

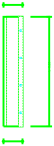

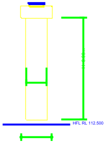

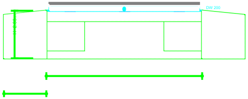

QA-ABT-CAP-DEF	Abutment cap depth	0 mm	>= 450 mm	OK
QA-ABT-CAP-PR(	Cap projection front/rear	0/0 mm	100-250 / 250-600 mm	OK
QA-DW-THK	Dirt wall thickness	0 mm	>= 250 mm	OK
QA-DW-TOP	Dirt wall to slab soffit	1.19 m	>= 0.30 m	OK
QA-DW-WEEP	Weep holes provided	4	1 per 3 m	OK
QA-ABT-OT	Overturning FOS	1.36	>= 1.40	FAIL
QA-ABT-SL	Sliding FOS	1.39	>= 1.40	FAIL
QA-ABT-BRG	Base pressure	159.91 kPa	<= 350.00 kPa	OK

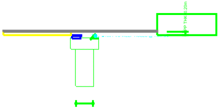

[illegible]

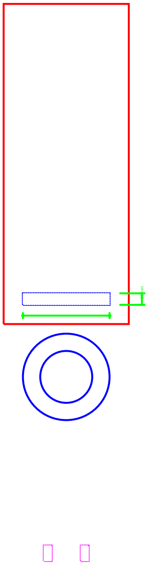
mm
GAP

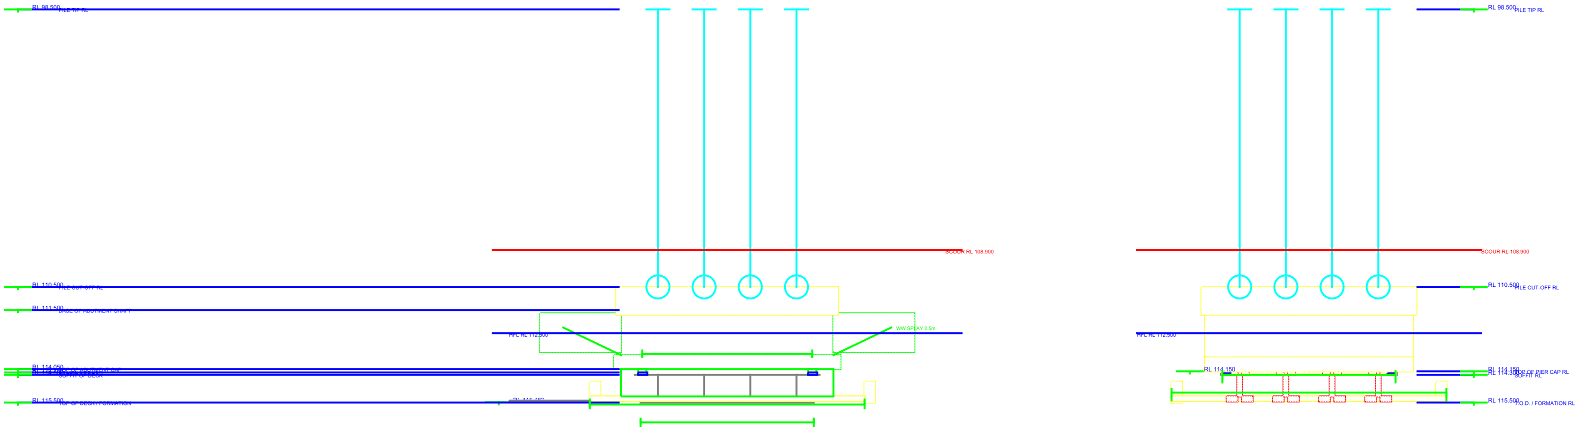
RL 98.500
PILE TIP RL
RL 110.500
PILE CUT-OFF RL
RL 111.500
BASE OF ABUTMENT SHAFT
RL 114.050
TOP OF ABUTMENT CAP
SOFFIT OF DECK
RL 115.500
TOP OF DECK / FORMATION
RL 115.482
HFL RL 112.500
SCOUR RL 108.900
WW SPLAY 2.5m
RL 98.500
PILE TIP RL
SCOUR RL 108.900
RL 110.500
PILE CUT-OFF RL
HFL RL 112.500
RL 114.150
RL 114.150
TOP OF PIER CAP RL
RL 114.300
SOFFIT RL
RL 115.500
T.O.D. / FORMATION RL

QA-ABT-CA	Abutment cap depth	0 mm	>= 450 mm	OK
QA-ABT-CA	Cap projection front/rear	0/0 mm	100-250 / 250-600 m	OK
QA-DW-THI	Dirt wall thickness	0 mm	>= 250 mm	OK
QA-DW-TOI	Dirt wall to slab soffit	1.19 m	>= 0.30 m	OK
QA-DW-WE	Weep holes provided	4	1 per 3 m	OK
QA-ABT-OT	Overturning FOS	1.36	>= 1.40	FAIL
QA-ABT-SL	Sliding FOS	1.39	>= 1.40	FAIL
QA-ABT-BR	Base pressure	159.91 kPa	<= 350.00 kPa	OK

(Not to Scale — indicative)