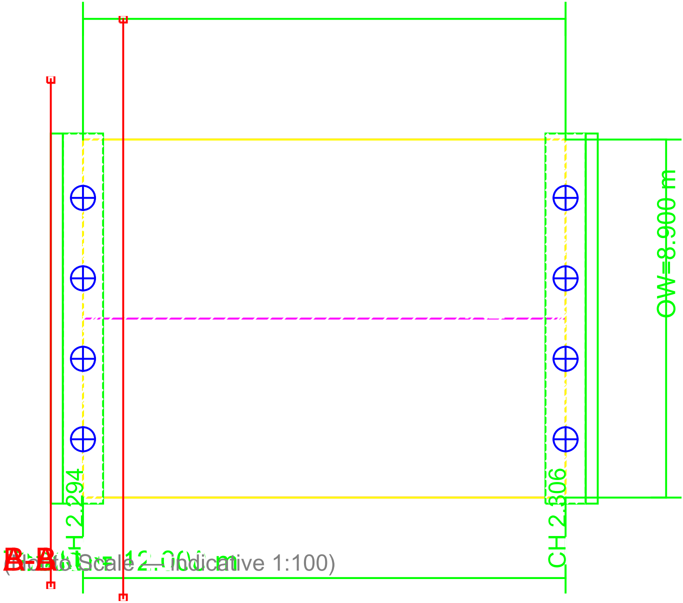
OW=8.900 m
CH 2.294
CH 2.306
A-A
B-B
12.000 m
(Not to Scale — indicative 1:100)

CONTINUOUS WEARING COAT OVER APPROACH SLABS

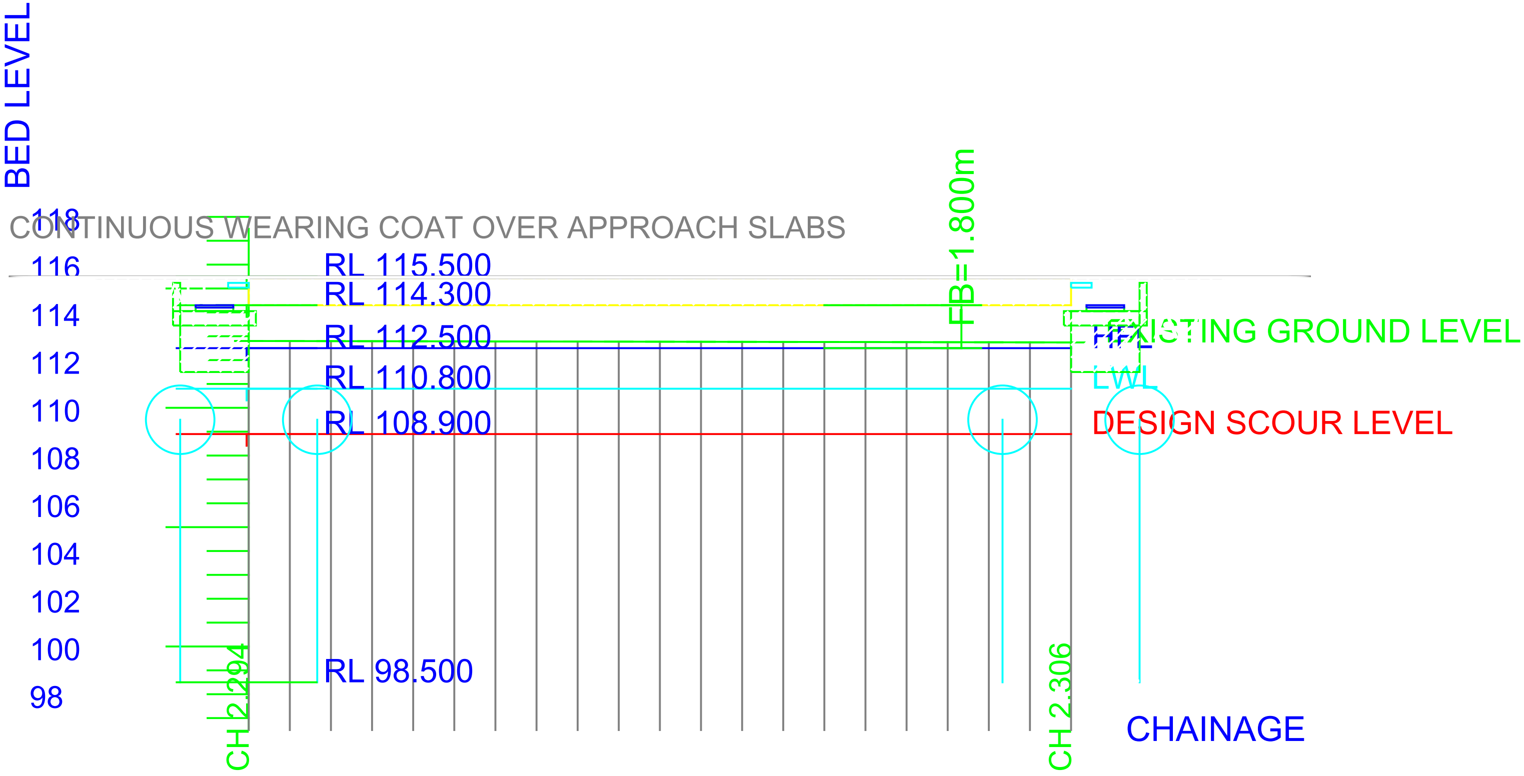
BED LEVEL
118
116
114
112
110
108
106
104
102
100
98
RL 115.500
RL 114.300
RL 112.500
RL 110.800
RL 108.900
RL 98.500
FB=1.800m
EXISTING GROUND LEVEL
HFL
LWL
DESIGN SCOUR LEVEL
CH 2.294
CH 2.306
CHAINAGE

(Not to Scale — indicative)

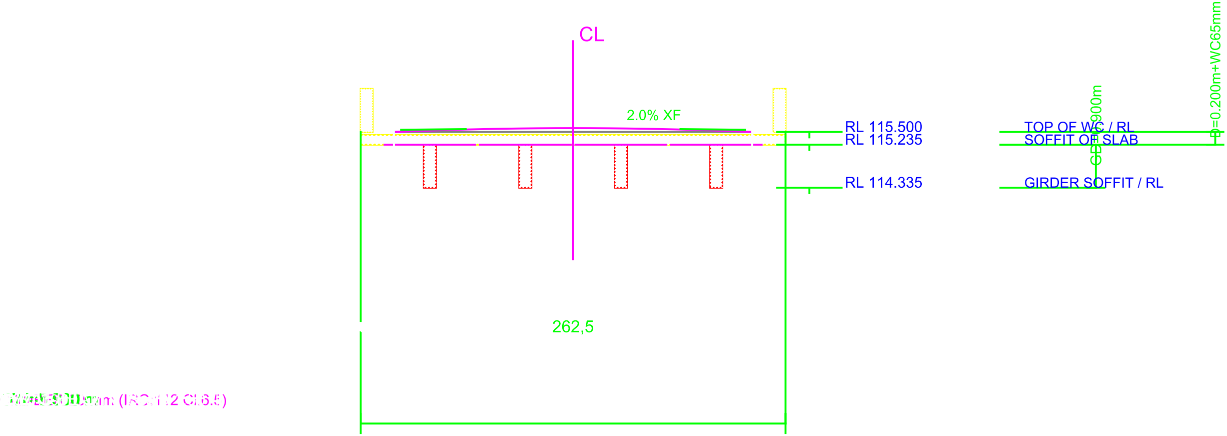
CL
2.0% XF
RL 115.500
RL 115.235
RL 114.335
TOP OF WC / RL
SOFFIT OF SLAB
GIRDER SOFFIT / RL
GD=0.900m
D=0.200m+WC65mm
262,5
mm (IRC:112 Cl.6.5)

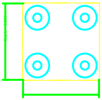

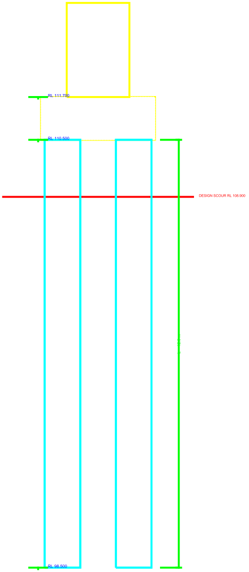
RL 111.700
RL 110.500
DESIGN SCOUR RL 108.900
RL 98.500

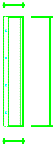

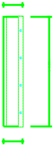

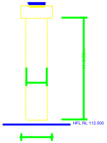

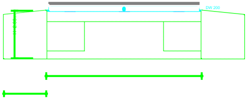

QA-ABT-CAP-DE	Abutment cap depth	0 mm	>= 450 mm	OK
QA-ABT-CAP-PR	Cap projection front/rear	0/0 mm	100-250 / 250-600 mm	OK
QA-DW-THK	Dirt wall thickness	0 mm	>= 250 mm	OK
QA-DW-TOP	Dirt wall to slab soffit	1.19 m	>= 0.30 m	OK
QA-DW-WEEP	Weep holes provided	4	1 per 3 m	OK
QA-ABT-OT	Overturning FOS	1.36	>= 1.40	FAIL
QA-ABT-SL	Sliding FOS	1.39	>= 1.40	FAIL
QA-ABT-BRG	Base pressure	159.91 kPa	<= 350.00 kPa	OK

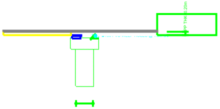

[illegible]

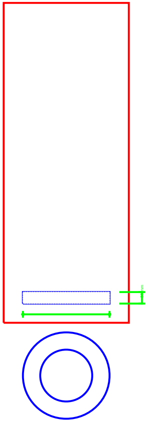

GAP

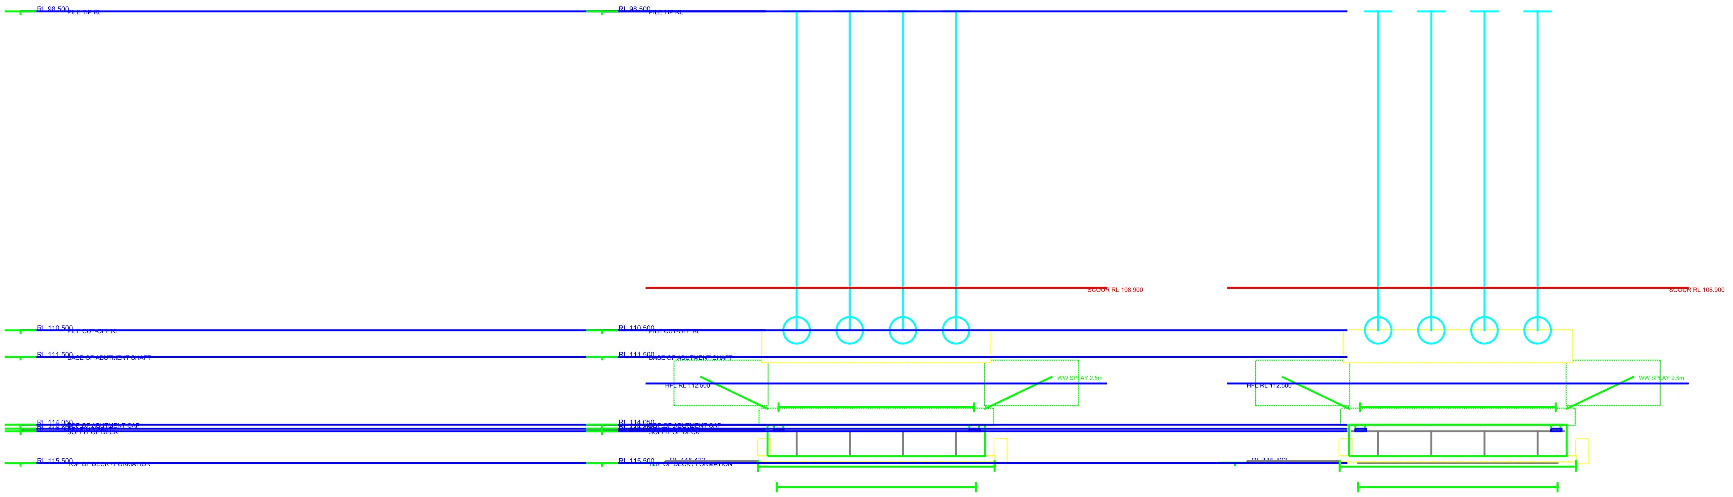
RL 98.500
PILE TIP RL
RL 98.500
PILE TIP RL
SCOUR RL 108.900
SCOUR RL 108.900
RL 110.500
PILE CUT-OFF RL
RL 110.500
PILE CUT-OFF RL
RL 111.500
BASE OF ABUTMENT SHAFT
RL 111.500
BASE OF ABUTMENT SHAFT
WW SPLAY 2.5m
WW SPLAY 2.5m
HFL RL 112.500
HFL RL 112.500
RL 114.050
TOP OF ABUTMENT CAP
SOFFIT OF DECK
RL 114.050
TOP OF ABUTMENT CAP
SOFFIT OF DECK
RL 115.500
TOP OF DECK / FORMATION
RL 115.500
RL 115.423
TOP OF DECK / FORMATION
RL 115.423

QA-ABT-C	Abutment cap depth	0 mm	>= 450 mm	OK
QA-ABT-C	Cap projection front/rear	0/0 mm	100-250 / 250-600 mm	OK
QA-DW-TH	Dirt wall thickness	0 mm	>= 250 mm	OK
QA-DW-TO	Dirt wall to slab soffit	1.19 m	>= 0.30 m	OK
QA-DW-W	Weep holes provided	4	1 per 3 m	OK
QA-ABT-C	Overturning FOS	1.36	>= 1.40	FAIL
QA-ABT-S	Sliding FOS	1.39	>= 1.40	FAIL
QA-ABT-B	Base pressure	159.91 kPa	<= 350.00 kPa	OK

(Not to Scale — indicative) TER (BEYOND)